


SIDE ELEVATION (SCALE NTS)

SEE DETAIL A


SEE DETAIL B

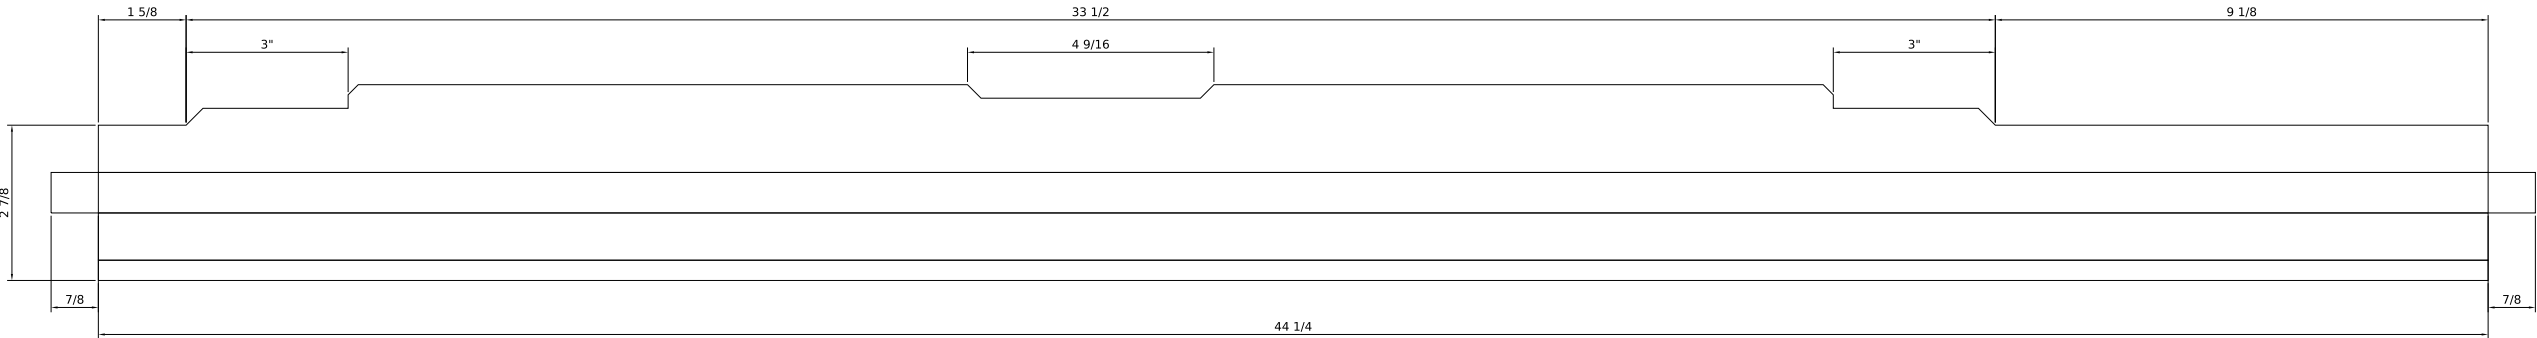

LAMINATED PANEL


UNITS: INCHES SOURCE: HAND SKETCH DATE: 2026-10-02

1. Transcribed from hand sketch. Verify before fabrication.
2. All dims in inches. Profile heights measured from top face of layer D.
3. $1\frac{5}{8} + 33\frac{1}{2} + 9\frac{1}{8} = 44\frac{1}{4}$: raised profile spans 33 1/2 at base.
4. 3" steps measured from profile start/end to the vertical riser.
5. Chamfer (0 -> 5/16) and slope (9/16 -> 3/4) assumed 45 deg.
6. Center notch: 4 9/16 wide, centered on profile, 1/4 deep (depth ASSUMED).
7. Core tenon 3/4 x 7/8 both ends, assumed flush with core faces.

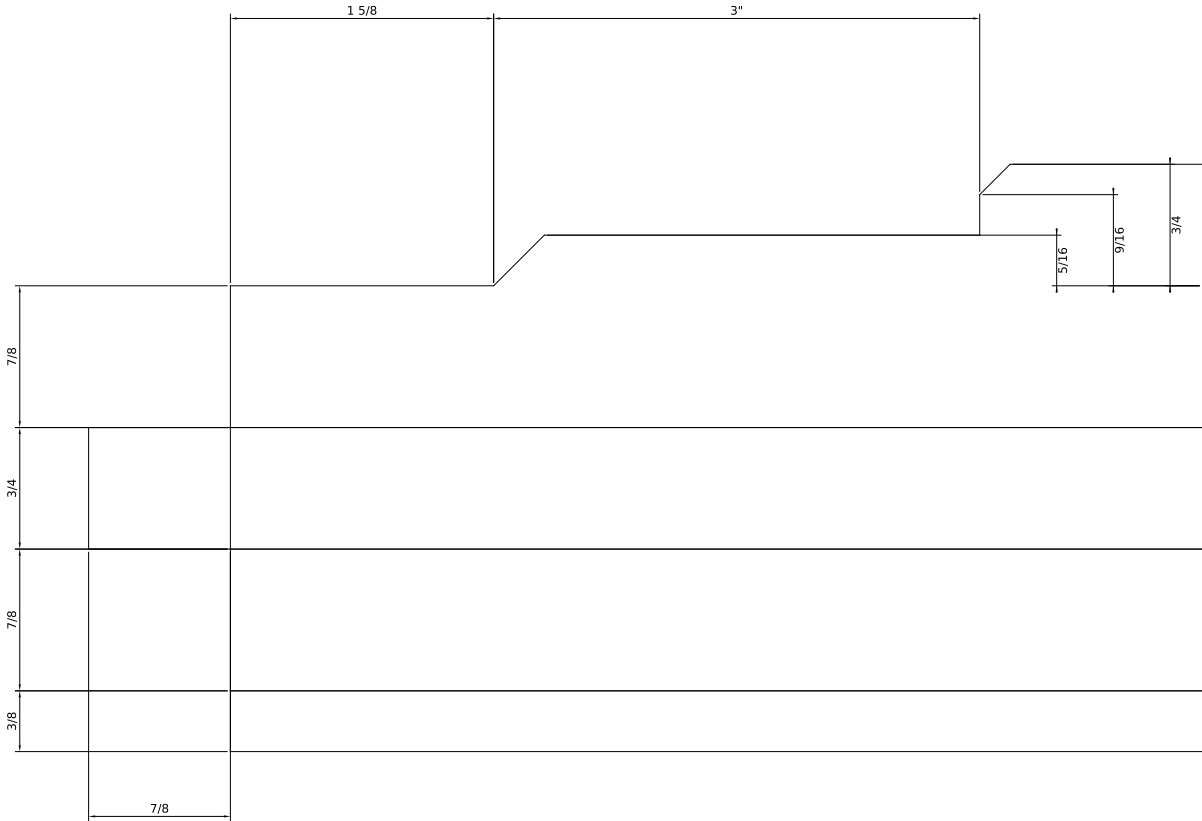

DETAIL A - LEFT END (SCALE 3:1)

Right end mirrors left end (9 1/8 from end to profile).

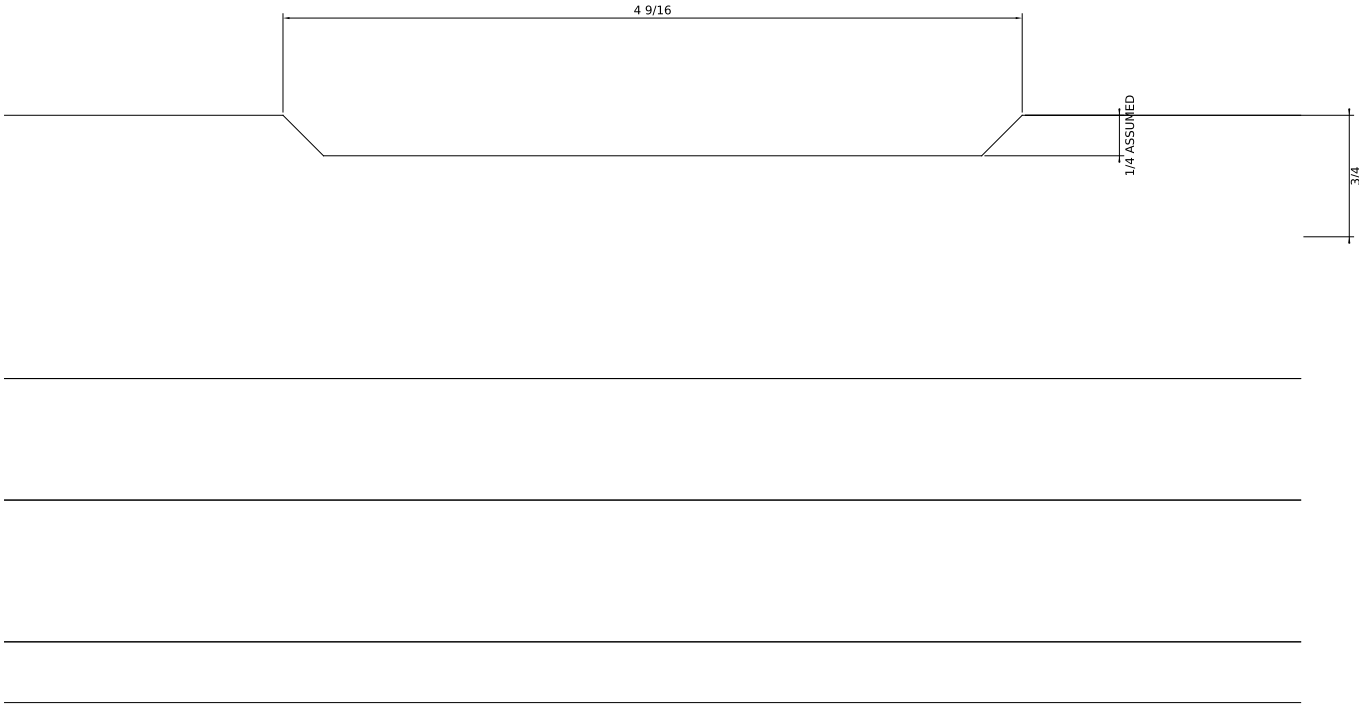

DETAIL B - CENTER NOTCH (SCALE 3:1)

Notch centered on 33 1/2 profile, 45 deg sides.